


DRAWING NUMBER MD-216-39AD-EG-CV-DED-1463 REV D01

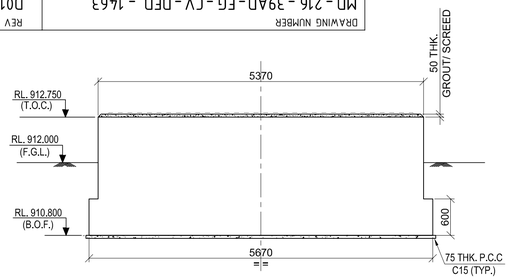


SECTION A-A
SCALE 1:50

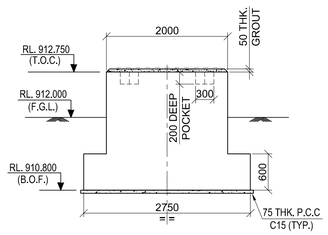


SECTION B-B
SCALE 1:50

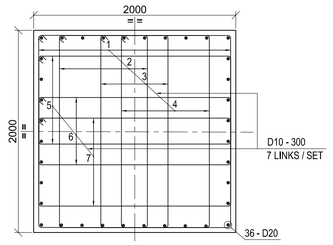


R.C DETAILS OF C2
SCALE 1:30

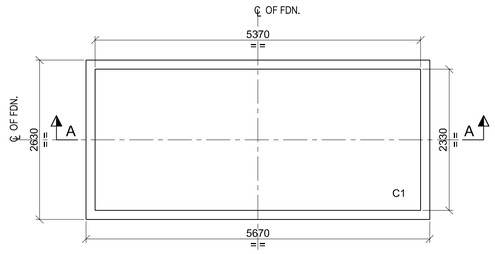


DETAILS OF FOUNDATION MKD. F1
SCALE 1:50

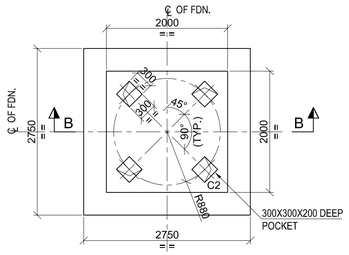


DETAILS OF FOUNDATION MKD. F2
SCALE 1:50

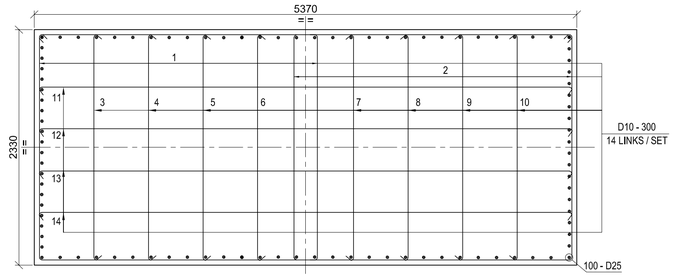


R.C DETAILS OF C1
SCALE 1:30

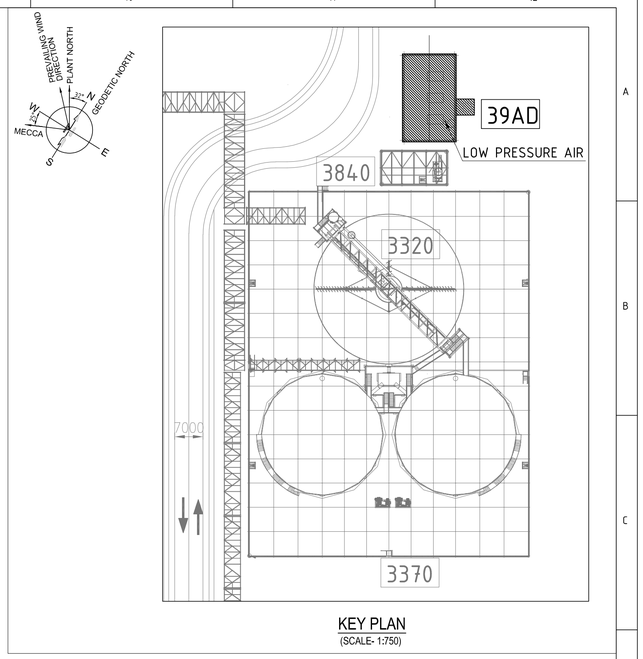


KEY PLAN
(SCALE- 1:750)

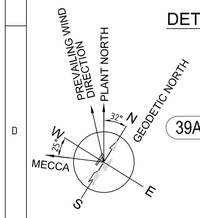


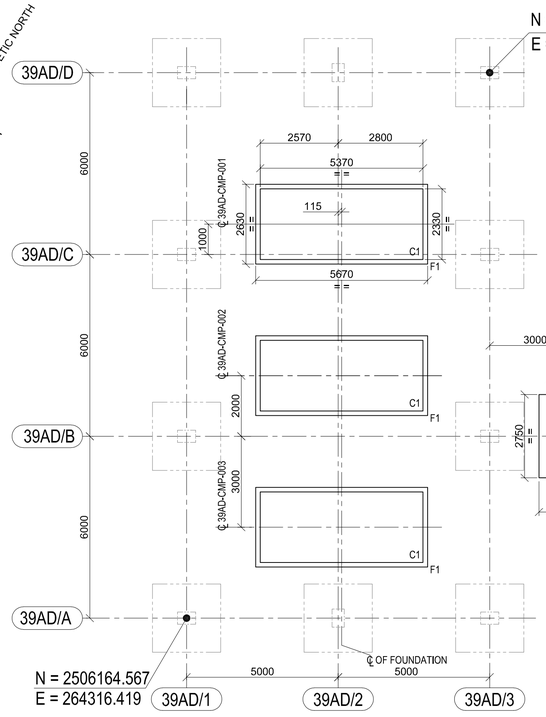


LAYOUT OF FOUNDATION
SCALE 1:100

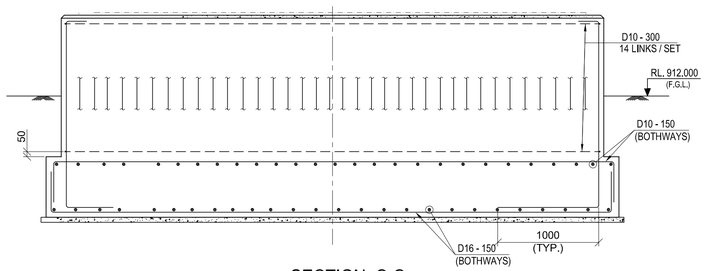


SECTION C-C
SCALE 1:30

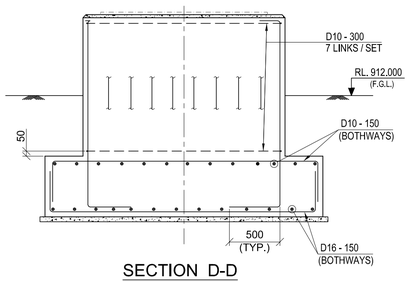

SECTION D-D
SCALE 1:30

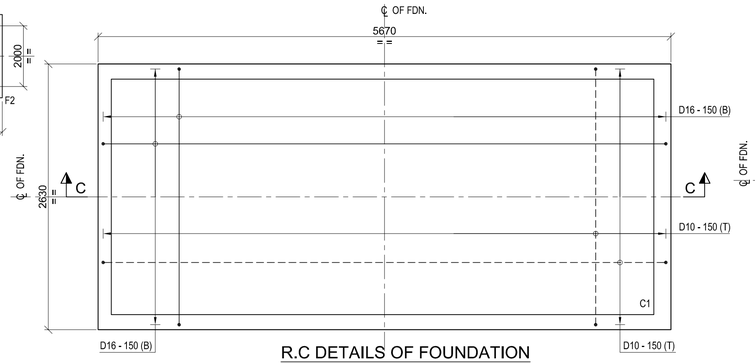

R.C DETAILS OF FOUNDATION MKD. F1
SCALE 1:30

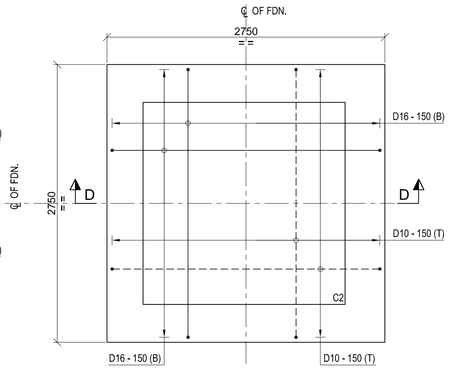

R.C DETAILS OF FOUNDATION MKD. F2
SCALE 1:30

LEGEND :-

R.L. - REDUCED LEVEL
T.O.C. - TOP OF CONCRETE.
F.G.L. - FINISHED GROUND LEVEL.
TYP. - TYPICAL.
P.C.C - PLAIN CEMENT CONCRETE
BOTTOM REINF.(B) - ————
TOP REINF.(T) - – – – – –
MKD. - MARKED
℄ - CENTRE LINE
B.O.F. - BOTTOM OF FOUNDATION
THK. - THICK
FDN. - FOUNDATION
R.C - REINFORCED CONCRETE
DIA - DIAMETER

NOTES :-

1. ALL DIMENSIONS ARE IN MILLIMETRES AND LEVELS AND CO-ORDINATES ARE IN METRES. UNLESS OTHERWISE STATED.
2. GRADE OF CONCRETE SHALL BE C35 (35MPa) FOR FOUNDATION & COLUMN.
3. GRADE OF REINFORCEMENT SHALL BE DEFORMED BAR ASTM A615 - GRADE 60 (fy = 420 MPa).
4. NET SAFE BEARING CAPACITY OF SOIL AT BOTTOM OF FOUNDATION IS CONSIDERED AS 350KN/SQ.M.
5. CLEAR COVER TO MAIN REINFORCEMENT SHALL BE AS FOLLOWS
 a) FOUNDATION = 50 mm (BOTTOM & SIDE) 50 mm, (TOP)
 b) COLUMN = 50mm
6. IF ANY PART OF FOUNDATION COMES ON BACKFILL ZONE OF ADJACENT FOUNDATION OR ANY LOOSE SOIL ARE ENCOUNTERED BELOW FOUNDATION LEVEL THE SAME SHALL BE REMOVED AND FILLED WITH PCC.
7. FOR STANDARD DETAILS OF ANCHOR BOLTS REFER DRG. NO MD-216-1000-EG-CV-DED-1003.
8. FOR STANDARD REINFORCEMENT DETAIL & GENERAL NOTES FOR CIVIL WORKS REFER DRAWING NO. MD-216-1000-EG-CV-DED-1005 &1001.

DOCUMENT NUMBER	REFERENCE DOCUMENTS	REV	DATE	REVISION DESCRIPTION	DRN	CHK	ENG	APP	EMP
MD-216-39AD-EG-ME-GAD-1002	GENERAL ARRANGEMENT DRAWING LOW PRESSURE AIR								
	PLAN VIEW	D01	05/05/2023	AS - BUILT	AUD	SJM	SOR	AG	
MD-216-39AD-EG-ME-GAD-1001	LOAD PLAN LOW PRESSURE AIR	C03	27/07/2021	ISSUED FOR CONSTRUCTION & REVISED AS MARKED C03	AUD	SJM	SOR	AG	
	PLAN VIEW	C02	25/11/2020	ISSUED FOR CONSTRUCTION & REVISED AS MARKED C02	AUD	SJM	SOR	AG	
MD-216-39AD-EG-CV-GAD-1001	CIVIL WORKS GUIDE DRAWING 39AD LOW PRESSURE AIR	C01	29/06/2020	ISSUED FOR CONSTRUCTION	SYA	SJM	SOR	AG	
	PLAN AT EL. +912.500	A01	27/05/2020	ISSUED FOR REFERENCE	SYA	SJM	SOR	AG	

RESERVED FOR VENDOR LOGO AND DRAWING NUMBER

LARSEN & TOUBRO

This drawing is the property of LARSEN & TOUBRO and must not be passed on to any person or body not authorized by us to receive it nor be copied or otherwise made use either in full or in part by such person or body without our prior permission in writing.

Outotec

The content of these documents are the sole property of Outotec Oyj. Any rights not expressly granted herein are reserved. Reproduction, transfer or distribution of part or all of the contents in any form without prior written permission of Outotec is prohibited.

MA'ADEN معادن
Saudi Arabian Mining Company شركة معادن العربية السعودية

This document and the information contained herein is Ma'aden proprietary know-how. This document or any part thereof should not be reproduced, stored in a retrieval system or transmitted by any means, electronic or otherwise, or divulged without prior written permission of Ma'aden.

LARSEN & TOUBRO DRAWING NUMBER: 019045_450_C_D_24192_001 — REVISION: 4
OUTOTEC DRAWING NUMBER: 900707__GAU01__AG10__CTB17__39501 — DOCUMENT ID: OU100685989 — REVISION: 4

DRAWN	SYA	25/05/2020
CHECKED	SJM	26/05/2020
ENGINEER	SOR	25/05/2020
APPROVED	AG	27/05/2020
EMPLOYER		

SCALE 1:50, 1:10 — A1

MANSOURAH - MASSARAH GOLD PROJECT
DETAIL DRAWING
LOW PRESSURE AIR
GA & RCC DETAILS OF PUMP FOUNDATIONS

DRAWING NUMBER: MD - 216 - 39AD - EG - CV - DED - 1463 — REV: D01