

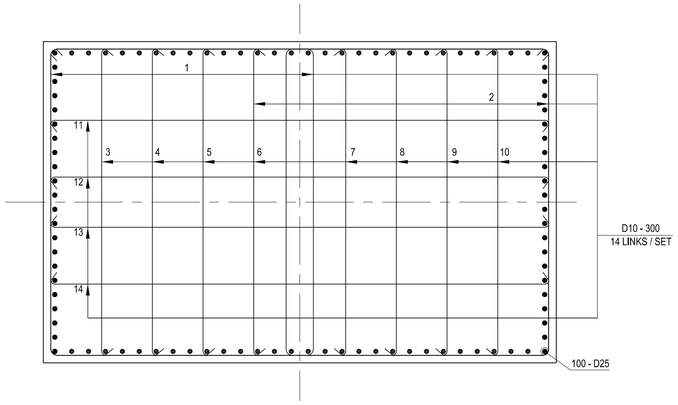



RCC. DETAIL OF C1
SCALE 1:20

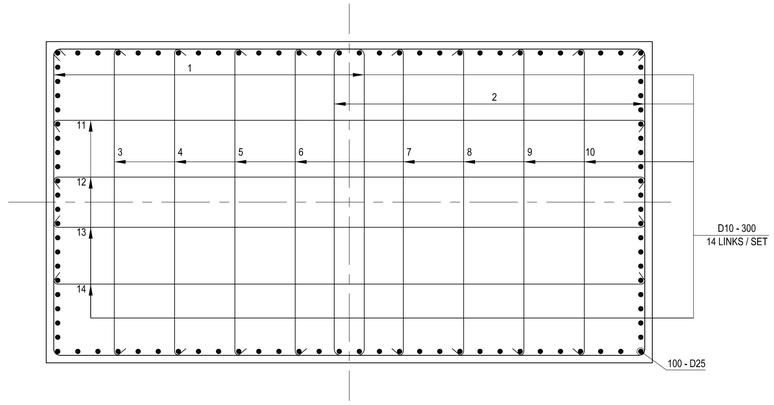


RCC. DETAIL OF C2
SCALE 1:20

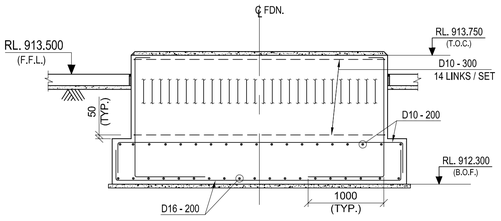


SECTION : A-A
SCALE 1:40

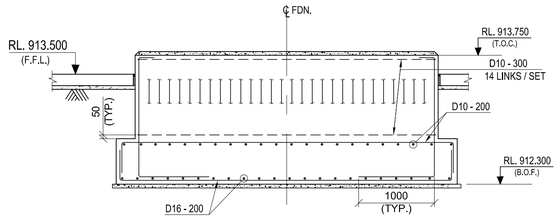

SECTION : B-B
SCALE 1:40

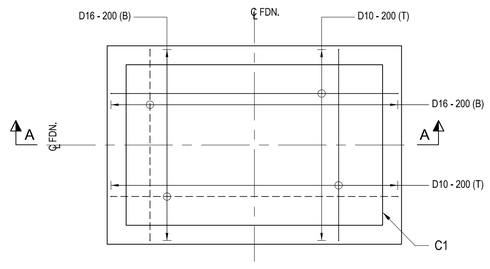

RCC. DETAIL OF FOUNDATION MKD F1
(FOR 3350-CMP-001,3350-CMP-002)
SCALE 1:40

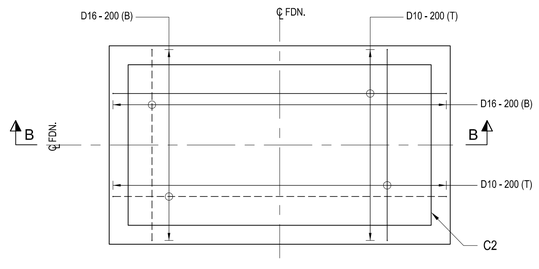

RCC. DETAIL OF FOUNDATION MKD F2
(39AB-CMP-001,39AB-CMP-002,39AB-CMP-003)
SCALE 1:40

LEGEND :-

R.L. - REDUCED LEVEL
℄ - CENTRE LINE
T.O.C. - TOP OF CONCRETE
F.G.L. - FINISHED GROUND LEVEL
F.F.L. - FINISHED FLOOR LEVEL
B.O.F. - BOTTOM OF FOUNDATION
TYP. - TYPICAL
R.C.C - REINFORCED CEMENT CONCRETE
P.C.C - PLAIN CEMENT CONCRETE
MKD. - MARKED
FDN. - FOUNDATION
THK. - THICK
T.O.G. - TOP OF GROUT
DET. - DETAIL
BOTTOM REINFORCEMENT (B) - - - - - - -
TOP REINFORCEMENT (T) - ———
DET. - DETAIL
FDN. - FOUNDATION
MKD - MARKED

NOTES:-

1. ALL DIMENSIONS ARE IN MILLIMETRES AND LEVELS AND CO-ORDINATES ARE IN METRES UNLESS OTHERWISE STATED.
2. GRADE OF CONCRETE SHALL BE C35 (35MPa) FOR FOUNDATION, C30 (30MPa) FOR GRADE SLAB & C15 (15MPa) FOR BLINDING CONCRETE.
3. GRADE OF REINFORCEMENT SHALL BE DEFORMED BAR 420 MPa (GRADE 60) - ASTM A615/A615M.
4. NET SAFE BEARING CAPACITY OF SOIL AT BOTTOM OF FOUNDATION IS CONSIDERED AS 350KN/ SQ. M.
5. CLEAR COVER TO REINFORCEMENT SHALL BE AS FOLLOWS
 a) FOUNDATION = 50 mm
 b) COLUMN = 50mm
6. FOR STANDARD REINFORCEMENT DETAIL & GENERAL NOTES FOR CIVIL WORKS REFER DRAWING NO. MD-216-1000-EG-CV-DED-1005 & 1001.

DOCUMENT NUMBER	REFERENCE DOCUMENTS	REV	DATE	REVISION DESCRIPTION	DRN	CHK	ENG	APP	EMP
MD-216-39AB-EG-CV-GAD-1459	HIGH PRESSURE AIR (BLOWER BUILDING)								
	LAYOUT & DETAILS OF FOUNDATION FOR AIR COMPRESSOR								
MD-216-3830-EG-ME-GAD-1017	FLOTATION REAGENTS, BLOWERS AND PLANT AIR	D01	04/05/2023	AS - BUILT	PML	SJM	SOR	AG	
	PLAN VIEW	C01	05/10/2020	ISSUED FOR CONSTRUCTION	PML	SJM	SOR	AG	
MD-216-3830-EG-CV-GAD-1002	3830 FLOTATION REAGENTS	A02	26/08/2020	REVISED AS PER EMPLOYER'S COMMENT ON 03/07/2020	PML	SJM	SOR	AG	
	PLAN AT EL. +913.500	A01	10/06/2020	ISSUED FOR REFERENCE	PML	SJM	SOR	AG	

RESERVED FOR VENDOR LOGO AND DRAWING NUMBER

LARSEN & TOUBRO

This drawing is the property of LARSEN & TOUBRO and must not be passed on to any person or body not authorized by us to receive it nor be copied or otherwise made use either in full or in part by such person or body without our prior permission in writing.

Outotec

The content of these documents are the sole property of Outotec Oyj. Any rights not expressly granted herein are reserved. Reproduction, transfer or distribution of part or all of the contents in any form without prior written permission of Outotec is prohibited.

MA'ADEN معادن
Saudi Arabian Mining Company شركة التعدين العربية السعودية

This document and the information contained herein is Ma'aden proprietary know-how. This document or any part thereof should not be reproduced, stored in a retrieval system or transmitted by any means, electronic or otherwise, or divulged without prior written permission of Ma'aden.

LARSEN & TOUBRO DRAWING NUMBER: 019045_450_C_D_24189_001 — REVISION: 3
OUTOTEC DRAWING NUMBER: 900707__GAU01__AG20__CTB17__39601 — DOCUMENT ID: OU100687752 — REVISION: 3

DRAWN	PML	04/06/2020
CHECKED	SJM	06/06/2020
ENGINEER	SOR	04/06/2020
APPROVED	AG	10/06/2020
EMPLOYER		
SCALE	1:75, 1:50, 1;20	A1

MANSOURAH - MASSARAH GOLD PROJECT
DETAIL DRAWING
HIGH PRESSURE AIR (BLOWER BUILDING)
RCC DETAILS OF FOUNDATION FOR AIR COMPRESSOR

DRAWING NUMBER: MD-216-39AB-EG-CV-DED-1460 — REV: D01