


SCALE 1:75

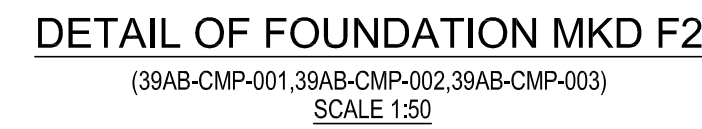

- R.L. - REDUCED LEVEL
C - CENTRE LINE
T.O.C. - TOP OF CONCRETE
TYP. - TYPICAL
T.O.G. - TOP OF GROUT
B.O.F. - BOTTOM OF FOUNDATION
F.G.L. - FINISHED GROUND LEVEL.
THK. - THICK
F.F.L. - FINISHED FLOOR LEVEL
P.C.C - PLAIN CEMENT CONCRETE
DET. - DETAIL
FDN. - FOUNDATION
MKD - MARKED
SQ - SQUARE

1. ALL DIMENSIONS ARE IN MILLIMETRES AND LEVELS AND CO-ORDINATES ARE IN METRES UNLESS OTHERWISE STATED.
2. NET SAFE BEARING CAPACITY OF SOIL AT BOTTOM OF FOUNDATION IS CONSIDERED AS 350KN/SQ. M.
3. GRADE OF CONCRETE SHALL BE C35 (35Mpa) FOR FOUNDATION, C30 (30Mpa) FOR GRADE SLAB & C15 (15Mpa) FOR BLINDING CONCRETE.
4. SAND SHALL BE COMPACTED TO A MINIMUM DEPTH OF 300MM TO ACHIEVE 98% MODIFIED MAXIMUM DRY DENSITY AS MEASURED BY ASTM D1557.
5. IF ANY PART OF FOUNDATION COMES ON BACKFILL ZONE OF ADJACENT FOUNDATION OR ANY LOOSE SOIL ARE ENCOUNTERED BELOW FOUNDATION LEVEL THE SAME SHALL BE REMOVED AND FILLED WITH PCC.
6. FOR STANDARD REFERENCE DRAWING DETAIL & GENERAL NOTES FOR CIVIL WORKS REFER DRAWING NO. MD-216-1000-EG-CV-DED-1005 & 1001.
7. FOR STANDARD DETAILS OF ANCHOR BOLTS REFER DRAWING NO MD-216-1000-EG-CV-DED-1003.

[illegible]

This drawing is the property of **LARSEN & TOUBRO** and must not be passed on to any person or body not authorized by us to receive it nor be copied or otherwise made use either in full or in part by such person or body without our prior permission in writing.

The content of these documents are the sole property of Outotec Oyj. Any rights not expressly granted herein are reserved. Reproduction, transfer or distribution of part or all of the contents in any form without prior written permission of Outotec is prohibited.

This document and the information contained herein is Ma'aden proprietary know-how. This document or any part thereof should not be reproduced, stored in a retrieval system or transmitted by any means, electronic or otherwise, or divulged without prior written permission of Ma'aden.

LARSEN & TOUBRO DRAWING NUMBER				REVISION
019045_450_C_G_24188_001				3
OUTOTEC DRAWING NUMBER			DOCUMENT ID	REVISION
900707 __GAU01 __AG520 __MTL01 __39603			OU100687750	3
DRAWN	PML	04/06/2020	MANSOURAH - MASSARAH GOLD PROJECT GENERAL ARRANGEMENT DRAWING HIGH PRESSURE AIR (BLOWER BUILDING) LAYOUT & DETAILS OF FDN. FOR AIR COMPRESSOR	
CHECKED	SJM	06/06/2020		
ENGINEER	SOR	04/06/2020		
APPROVED	AG	10/06/2020		
EMPLOYER			DRAWING NUMBER	REV
SCALE	1:75, 1:50, 1:20	A1	MD - 216 - 39AB- EG - CV - GAD - 1459	D01