


DRAWING NUMBER MD-216-39EJ-EG-CV-DED-1458 REV D01

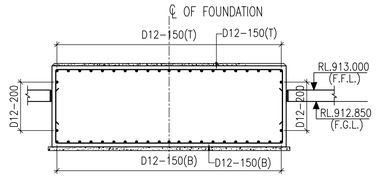


SECTION 13-13
(SC1ALE 1:40)

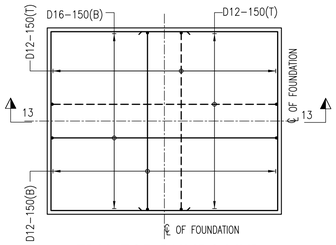


FDN. FOR PUMPS MKD.
39EJ-PMP-206, 207 & 208
(SC1ALE 1:40)

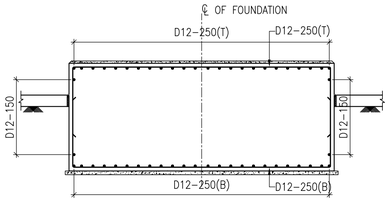


SECTION 5-5
(SCALE 1:40)

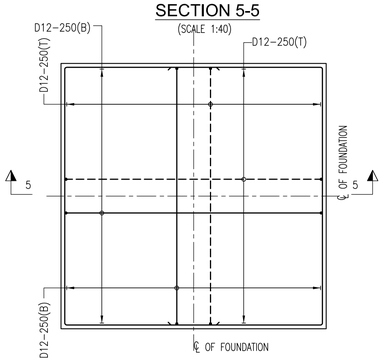


DETAIL FOR FOUNDATION MKD.
39EJ-TNK-201
(SCALE 1:40)

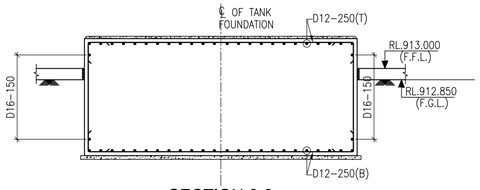


SECTION 6-6
(SCALE 1:40)

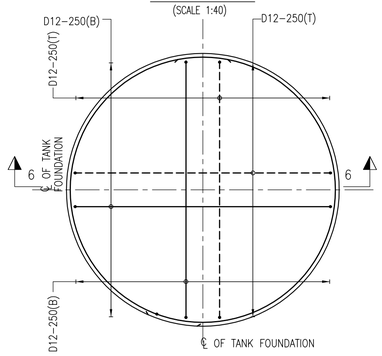


DETAIL FOR TANK FOUNDATION MKD.
39EJ-PKJ-203 & 204
(SCALE 1:40)

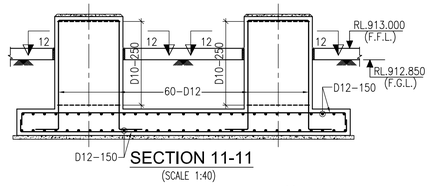


SECTION 11-11
(SCALE 1:40)

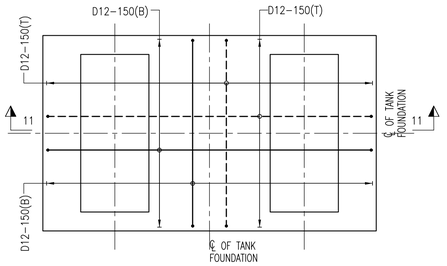


DETAIL FOR TANK FOUNDATION MKD.
39EJ-TNK-205 & 206
(SCALE 1:40)

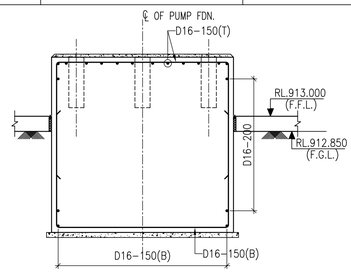


SECTION 1-1
(SCALE 1:30)

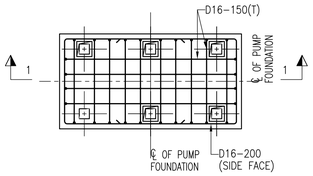


FDN. FOR PUMP MKD.
39EJ-PMP-001, 002 & 003
(SCALE 1:30)

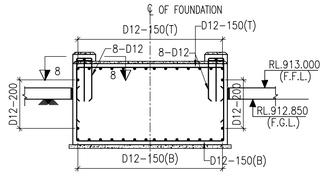


SECTION 7-7
(SCALE 1:40)

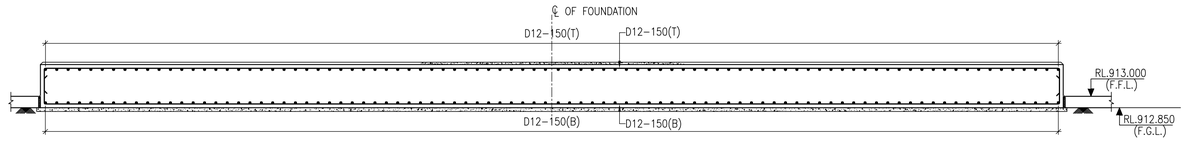


SECTION 10-10
(SCALE 1:40)

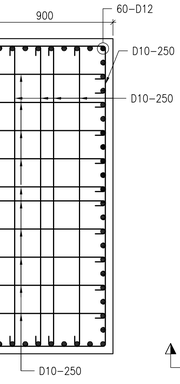


SECTION 12-12
(SCALE 1:20)

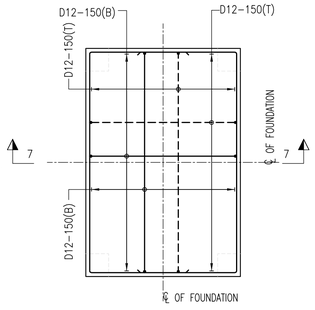


FDN. FOR BLOWER MKD.
39EJ-BLW-201 & 202
(SCALE 1:40)

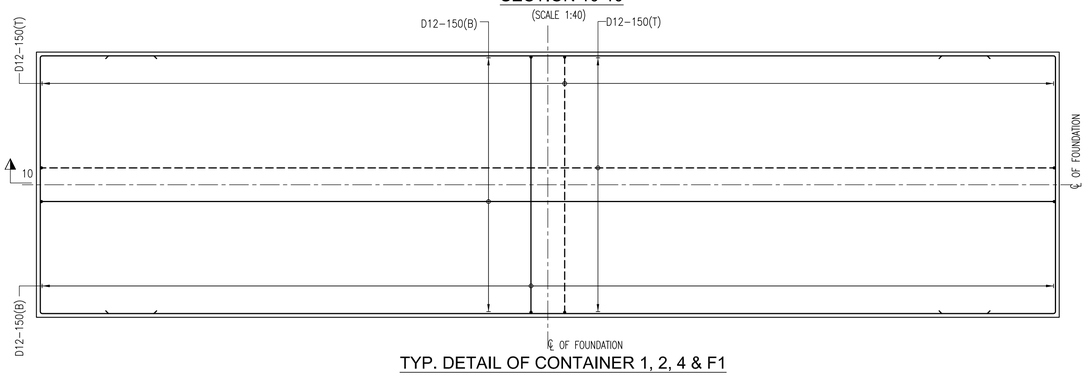


TYP. DETAIL OF CONTAINER 1, 2, 4 & F1
(SCALE 1:40)

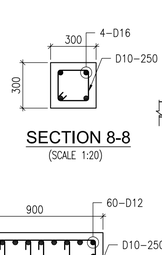


SECTION 8-8
(SCALE 1:20)

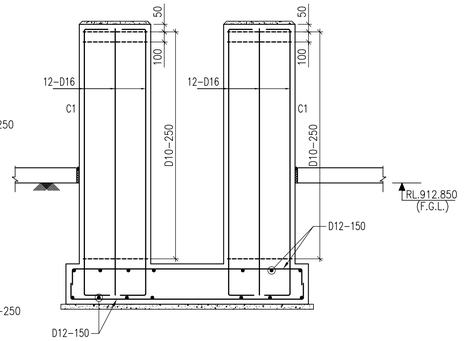

SECTION 2-2
(SCALE 1:30)

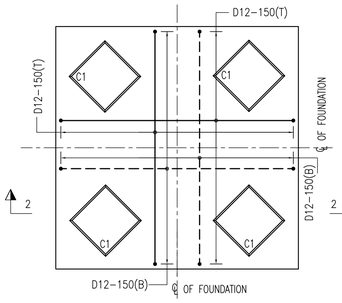

RC. DETAIL FOR FOUNDATION MKD.
39EJ-PKG-205, 206 & 207
(SCALE 1:30)

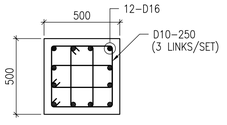

RC. DETAIL OF C1
(SCALE 1:20)

LEGEND :-

R.L. – REDUCED LEVEL
℄ – CENTRE LINE
T.O.C. – TOP OF CONCRETE
TYP. – TYPICAL
F.G.L. – FINISHED GROUND LEVEL
F.F.L. – FINISHED FLOOR LEVEL
B.O.F. – BOTTOM OF FOUNDATION
MKD. – MARKED
P.C.C – PLAIN CEMENT CONCRETE
DET. – DETAIL
BOTTOM REINFORCEMENT (B) - - - - - - - -
TOP REINFORCEMENT (T) ————————
SQ. – SQUARE
R.C. – REINFORCED CONCRETE
FDN. – FOUNDATION
THK. – THICK
REINF. –REINFORCED

NOTES:-

1. ALL DIMENSIONS ARE IN MILLIMETRES AND LEVELS AND CO-ORDINATES ARE IN METRES UNLESS OTHERWISE STATED.
2. NET SAFE BEARING CAPACITY OF SOIL AT BOTTOM OF FOUNDATION CONSIDER 200KN/ SQ. M
3. GRADE OF CONCRETE SHALL BE C35 (35MPa) FOR FOUNDATION & C15 (15MPa) FOR BLINDING CONCRETE.
4. GRADE OF REINFORCEMENT SHALL BE DEFORMED BAR 420 MPa (GRADE 60) – ASTM A615/A615M.
5. IF ANY PART OF FOUNDATION COMES ON BACKFILL ZONE OF ADJACENT FOUNDATION OR ANY LOOSE SOIL ARE ENCOUNTERED BELOW FOUNDATION LEVEL THE SAME SHALL BE REMOVED AND FILLED WITH PCC (C15).
6. CLEAR COVER TO REINFORCEMENT SHALL BE a. FOUNDATIONS = 50 MM., b. COLUMNS = 50 MM.
7. FOR STANDARD REINFORCEMENT DETAIL & GENERAL NOTES FOR CIVIL WORKS REFER DRAWING NO. MD-216-1000-EG-CV-DED-1005 & 1001.

DOCUMENT NUMBER	REFERENCE DOCUMENTS	REV	DATE	REVISION DESCRIPTION	DRN	CHK	ENG	APP	EMP
		D01	05/05/2023	AS - BUILT	ABS	SJM	AVG	AG	
		C02	19/01/2021	ISSUED FOR CONSTRUCTION & REVISED AS MKD. △C02	ABS	SJM	AVG	AG	
		C01	21/12/2020	ISSUED FOR CONSTRUCTION	SC	TG	AVG	AG	
MD-216-39EJ-EG-CV-GAD-1458	GA. DETAILS OF FOUNDATION	A01	19/10/2020	ISSUED FOR REFERENCE	SC	TG	AVG	AG	

RESERVED FOR VENDOR LOGO AND DRAWING NUMBER

LARSEN & TOUBRO

This drawing is the property of LARSEN & TOUBRO and must not be passed on to any person or body not authorized by us to receive it nor be copied or otherwise made use either in full or in part by such person or body without our prior permission in writing.

Outotec

The content of these documents are the sole property of Outotec Oyj. Any rights not expressly granted herein are reserved. Reproduction, transfer or distribution of part or all of the contents in any form without prior written permission of Outotec is prohibited.

MA'ADEN معادن
Saudi Arabian Mining Company شركة المعادن العربية السعودية

This document and the information contained herein is Ma'aden proprietary know-how. This document or any part thereof should not be reproduced, stored in a retrieval system or transmitted by any means, electronic or otherwise, or divulged without prior written permission of Ma'aden.

LARSEN & TOUBRO DRAWING NUMBER: 019045_450_C_D_24433_001 — REVISION: 3
OUTOTEC DRAWING NUMBER: 900707 _GAU01 _AG36_CTB17 _39303 — DOCUMENT ID: OU100703851 — REVISION: 3

DRAWN	SC	12/10/2020
CHECKED	TG	13/10/2020
ENGINEER	AVG	12/10/2020
APPROVED	AG	19/10/2020
EMPLOYER		
SCALE	1:20, 1:50, 1:150	A1

MANSOURAH - MASSARAH GOLD PROJECT
DETAIL DRAWING
DEMINERALIZATION SYSTEM
RCC DETAILS OF FOUNDATION

DRAWING NUMBER: MD-216-39EJ-EG-CV-DED-1458 — REV: D01