DRAWING NUMBER MD-216-39AB-EG-CV-GAD-1465 REV D01

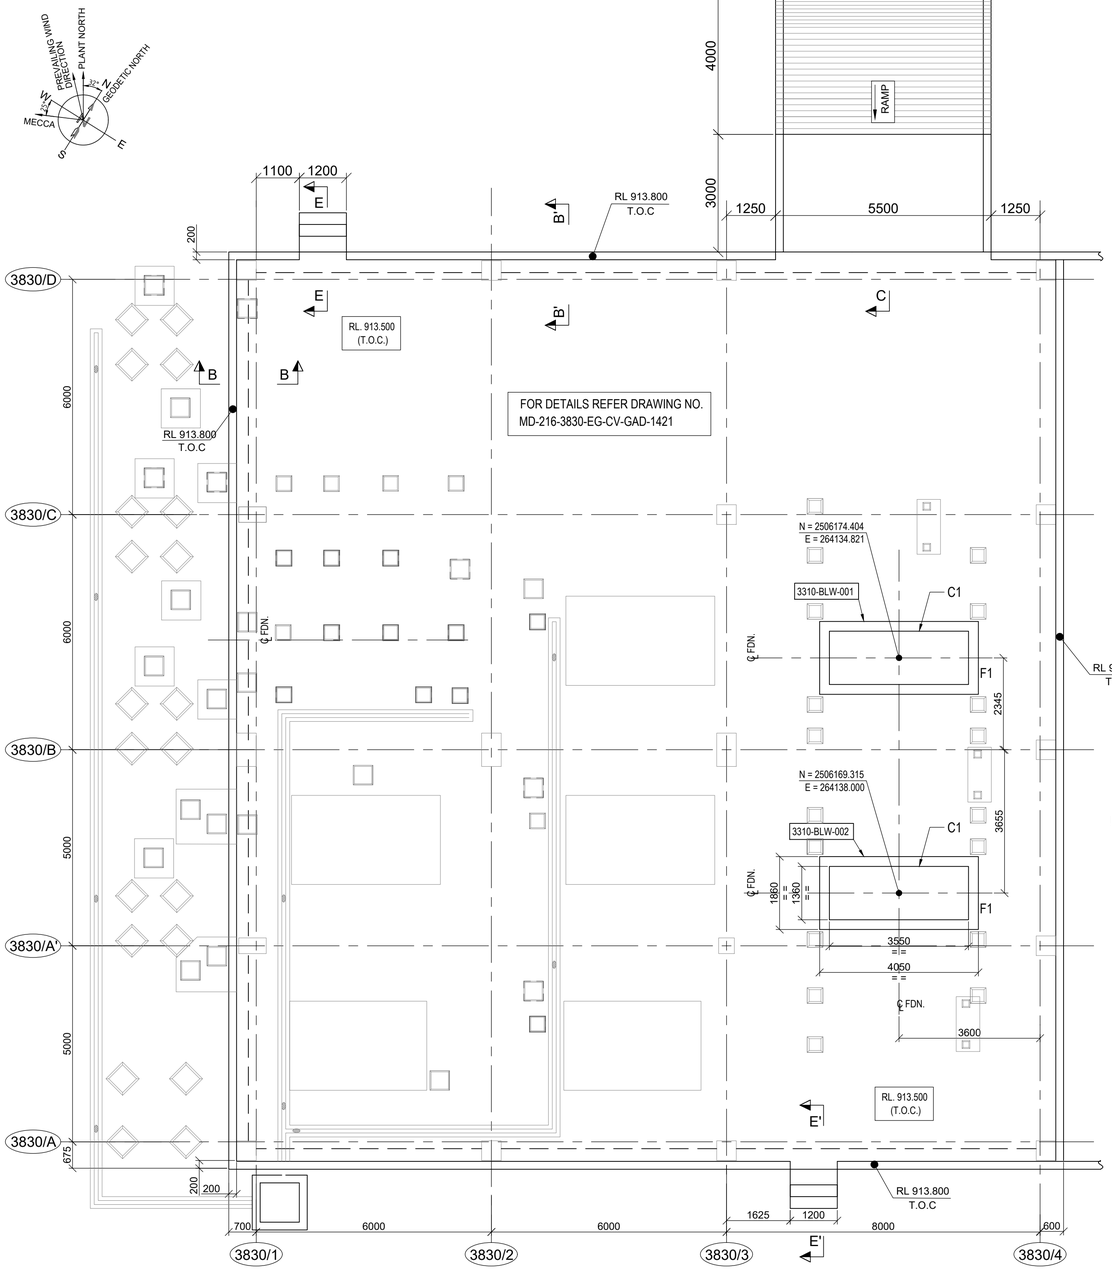

LAYOUT OF FOUNDATION
SCALE 1:75

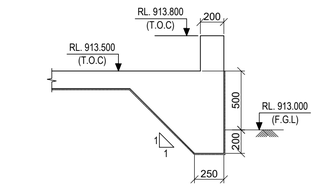

SECTION B'-B'
SCALE 1:25

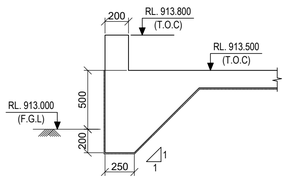

SECTION B-B
SCALE 1:25

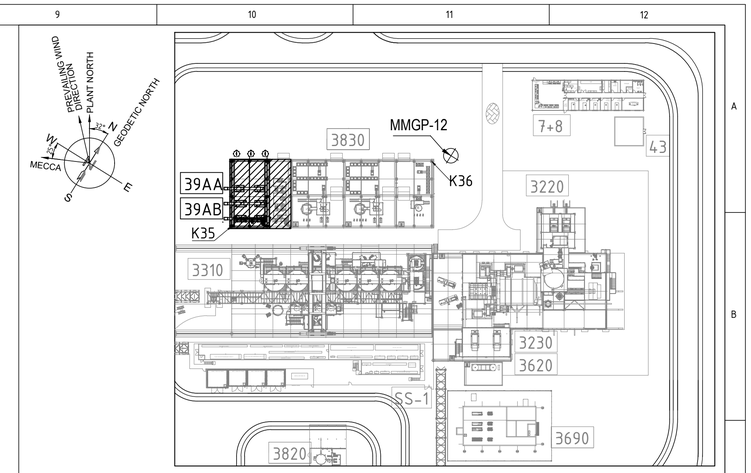

KEY PLAN
SCALE 1:1000

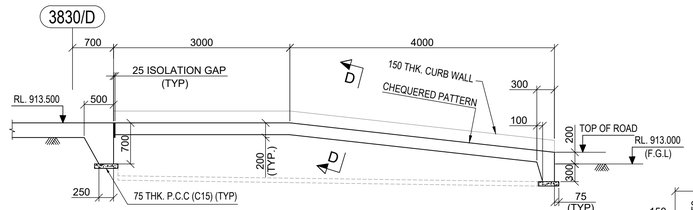

SECTION C-C
SCALE 1:50

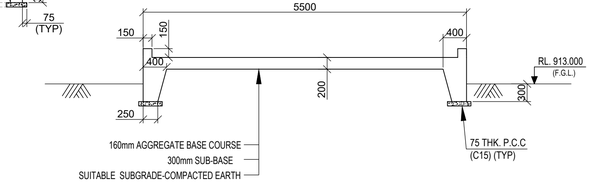

SECTION D-D
SCALE 150

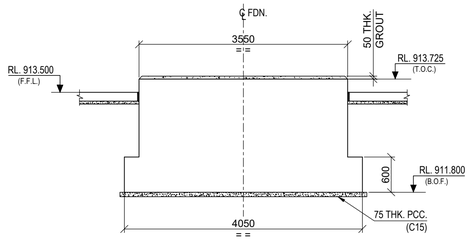

SECTION A-A
SCALE 1:50

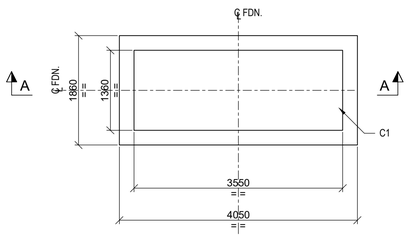

DETAIL OF FOUNDATION MKD F1
(FOR 3310-BLW-001 & 3310-BLW-002)
SCALE 1:50

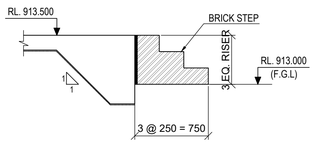

SECTION E-E
SECTION E'-E' (OPPOSITE HAND)
SCALE 1:30

LEGEND :-

R.L. - REDUCED LEVEL
℄ - CENTRE LINE.
T.O.C. - TOP OF CONCRETE
TYP. - TYPICAL
T.O.G. - TOP OF GROUT
B.O.F. - BOTTOM OF FOUNDATION
F.G.L. - FINISHED GROUND LEVEL.
THK. - THICKNESS
F.F.L. - FINISHED FLOOR LEVEL
P.C.C. - PLAIN CEMENT CONCRETE
DET. - DETAIL
FDN. - FOUNDATION
MKD. - MARKED

NOTES:-

1. ALL DIMENSIONS ARE IN MILLIMETRES AND LEVELS AND CO-ORDINATES ARE IN METRES UNLESS OTHERWISE STATED.
2. NET SAFE BEARING CAPACITY OF SOIL AT BOTTOM OF FOUNDATION IS CONSIDERED AS 350KN/ SQ. M.
3. GRADE OF CONCRETE SHALL BE C35 (35Mpa) FOR FOUNDATION, C30 (30Mpa) FOR GRADE SLAB & C15 (15Mpa) FOR BLINDING CONCRETE.
4. IF ANY PART OF FOUNDATION COMES ON BACKFILL ZONE OF ADJACENT FOUNDATION OR ANY LOOSE SOIL ARE ENCOUNTERED BELOW FOUNDATION LEVEL THE SAME SHALL BE REMOVED AND FILLED WITH PCC.
5. FOR STANDARD REINFORCEMENT DETAIL & GENERAL NOTES FOR CIVIL WORKS REFER DRAWING NO. MD-216-1000-EG-CV-DED-1005 & 1001.
6. FOR STANDARD DETAILS OF ANCHOR BOLTS REFER DRAWING NO MD-216-1000-EG-CV-DED-1003.
7. FOR DETAILS OF GRADE SLAB REFER DRAWING NO. MD-216-1000-EG-CV-DED-1002.

DOCUMENT NUMBER	REFERENCE DOCUMENTS	REV	DATE	REVISION DESCRIPTION	DRN	CHK	ENG	APP	EMP
MD-216-39AB-EG-CV-DED-1466	PLANT AIR RCC DETAILS OF FOUNDATION								
MD-216-39AB-EG-CV-GAD-1459	HIGH PRESSURE AIR (BLOWER BUILDING)								
	LAYOUT & DETAILS OF FDN. FOR AIR COMPRESSOR	D01	04/05/2023	AS - BUILT	SYA	SJM	SOR	AG	
MD-216-3830-EG-ME-GAD-1017	FLOTATION REAGENTS, BLOWERS AND PLANT AIR	C03	17/03/2021	ISSUED FOR CONSTRUCTION & REVISED AS MARKED C03	SYA	SJM	SOR	AG	
	PLAN VIEW	C02	20/01/2021	ISSUED FOR CONSTRUCTION & REVISED AS MARKED C02	SYA	SJM	SOR	AG	
MD-216-3830-EG-CV-GAD-1002	3830 FLOTATION REAGENTS	C01	08/08/2020	ISSUED FOR CONSTRUCTION	SYA	SJM	SOR	AG	
	PLAN AT EL. +913.500	A01	08/07/2020	ISSUED FOR REFERENCE	SYA	SJM	SOR	AG	

RESERVED FOR VENDOR LOGO AND DRAWING NUMBER

LARSEN & TOUBRO

This drawing is the property of LARSEN & TOUBRO and must not be passed on to any person or body not authorized by us to receive it nor be copied or otherwise made use either in full or in part by such person or body without our prior permission in writing.

Outotec

The content of these documents are the sole property of Outotec Oy. Any rights not expressly granted herein are reserved. Reproduction, transfer or distribution of part or all of the contents in any form without prior written permission of Outotec is prohibited.

MA'ADEN معادن
Saudi Arabian Mining Company شركة المعادن العربية السعودية

This document and the information contained herein is Ma'aden proprietary know-how. This document or any part thereof should not be reproduced, stored in a retrieval system or transmitted by any means, electronic or otherwise, or divulged without prior written permission of Ma'aden.

LARSEN & TOUBRO DRAWING NUMBER: O19045_450_C_G_24194_001 — REVISION: 4
OUTOTEC DRAWING NUMBER: 900707 _GAU01 _AG20_MTL01 _39604 — DOCUMENT ID: OU100687751 — REVISION: 4

DRAWN	SYA	06/07/2020
CHECKED	SJM	07/07/2020
ENGINEER	SOR	06/07/2020
APPROVED	AG	08/07/2020
EMPLOYER		
SCALE	1:75, 1:50, 1;20	A1

MANSOURAH - MASSARAH GOLD PROJECT
GENERAL ARRANGEMENT DRAWING
PLANT AIR
LAYOUT & DETAILS OF FOUNDATION

DRAWING NUMBER: MD - 216 - 39AB - EG - CV - GAD - 1465 — REV: D01